



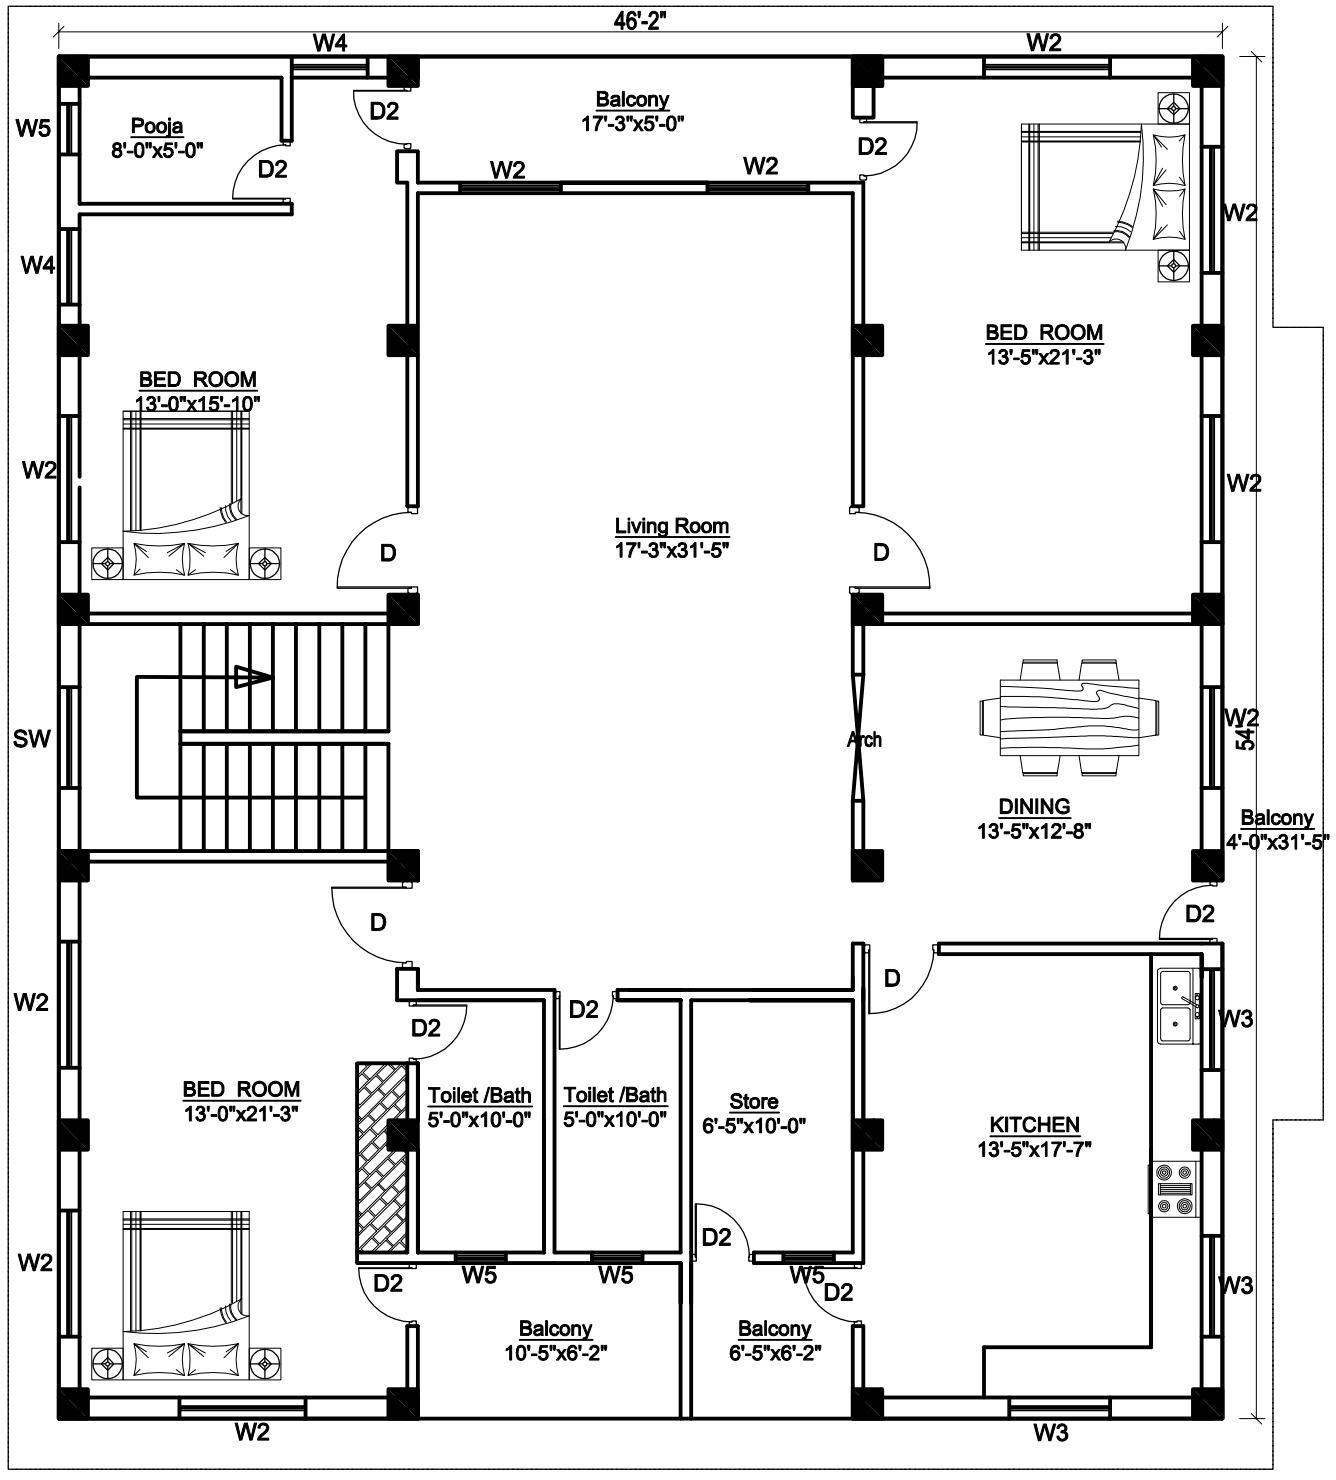

DOORS AND WINDOWS SCHEDULE						
S.NO.	SYMBOL	DESCRIPTION	DIMENSION	NOs. GROUND FLOOR	WOOD SIZE	TOTAL
1.	D	DOOR	3'-6"X7'-0"	4	3"x4"	5.83
2.	D2	DOOR	2'-6"X7'-0"	10	3"x4"	13.75
3.	W2	WINDOW	6'-0"X4'-6"	10	3"x5"	33.33
4.	W3	WINDOW	4'-0"X3'-6"	3	3"x5"	5.78
5.	W4	WINDOW	3'-0"X4'-6"	3	3"x5"	6.09
6.	W5	WINDOW	3'-0"X2'-6"	4	3"x5"	4.50
7.	SW	WINDOW	4'-0"X4'-0"	1	3"x4"	2.00
					Total = 71.28 cft	

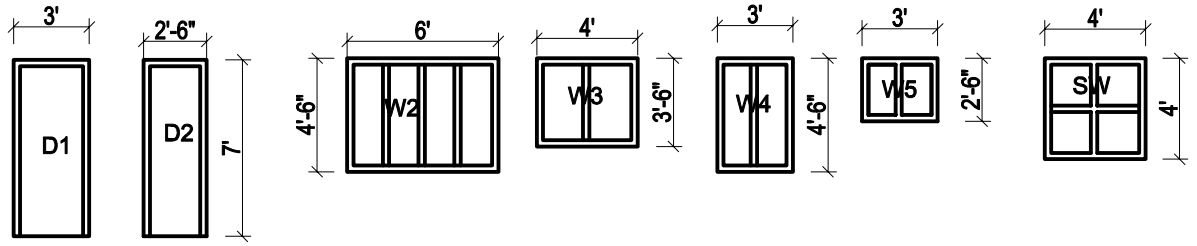

FIRST FLOOR PLAN revised

FLOOR AREA =2492.31 SQ.FT.

Prepared By :

In Technical Assistance with

RK ENGINEERING CONSULTANT

Rajbiraj-02, Saptari

Mobile : 9852820215,9825723935