

Owner : Mrs. Sudha Kumari singh
at
Rajbiraj-05

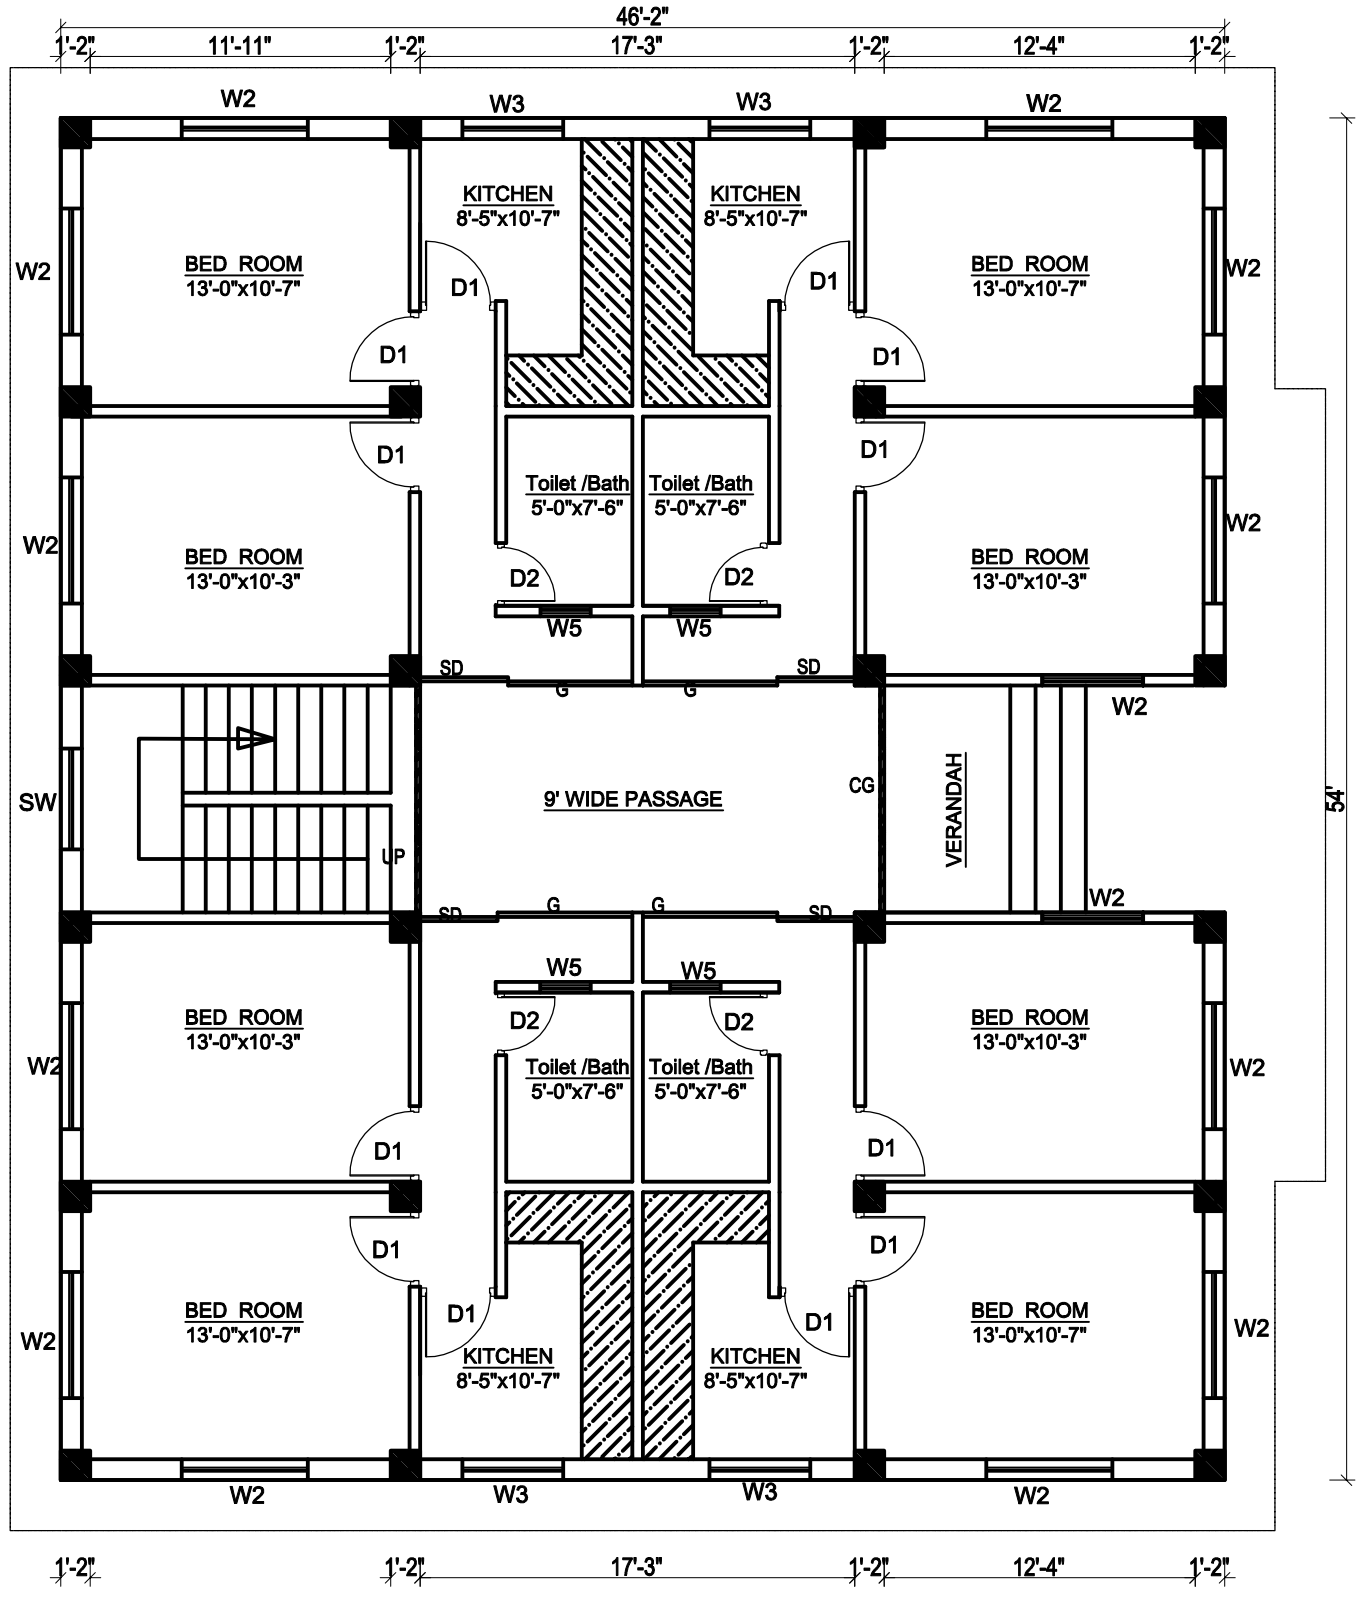

DOORS AND WINDOWS SCHEDULE						
S.NO.	SYMBOL	DESCRIPTION	DIMENSION	NOs. GROUND FLOOR	WOOD SIZE	TOTAL
1.	D1	DOOR	3'-0"X7'-0"	12	3"x4"	17.00
2.	D2	DOOR	2'-6"X7'-0"	4	3"x4"	5.5
3.	W2	WINDOW	6'-0"X4'-6"	14	3"x5"	50.31
4.	W3	WINDOW	4'-0"X3'-6"	4	3"x5"	7.70
5.	W5	WINDOW	3'-0"X2'-6"	4	3"x5"	4.50
6.	SW	WINDOW	4'-0"X4'-0"	1	3"x4"	2.00
7.						
					Total = 87.01 cft	

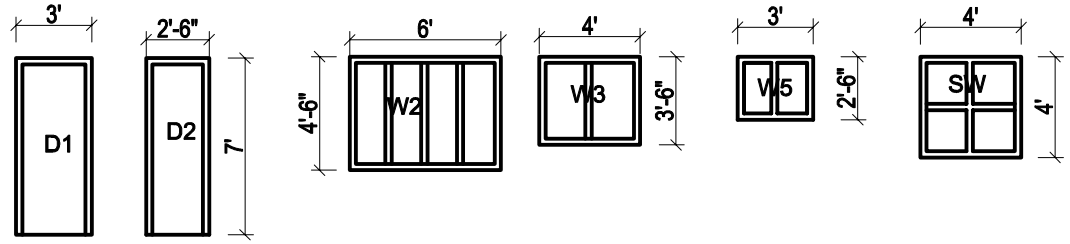

GROUND FLOOR PLAN

FLOOR AREA =2492.31 SQ.FT.

Prepared By :

In Technical Assistance with

RK ENGINEERING CONSULTANT

Rajbiraj-02, Saptari
Mobile : 9852820215,9825723935